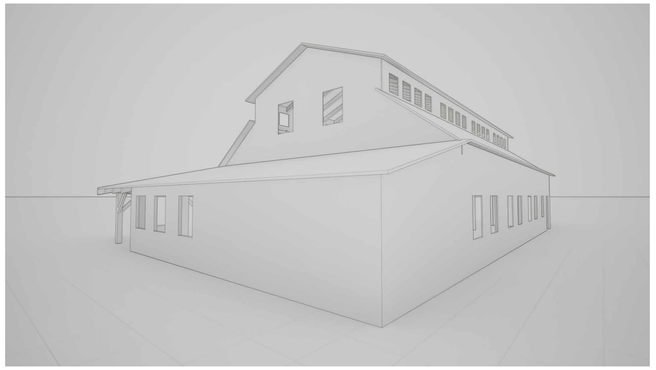

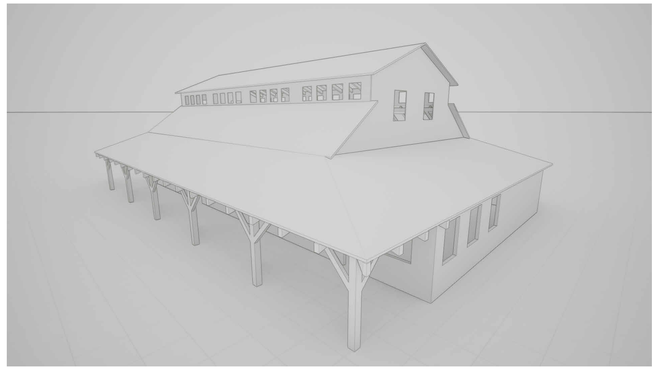

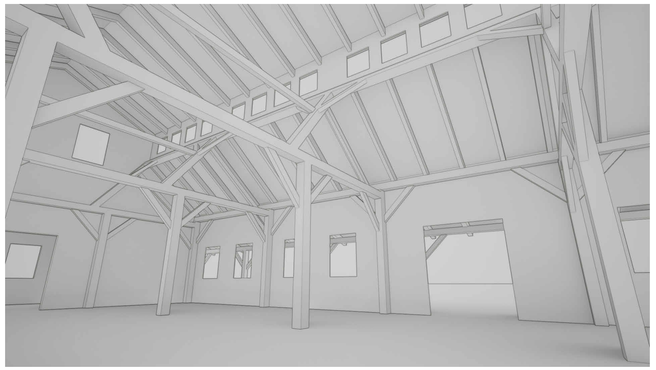

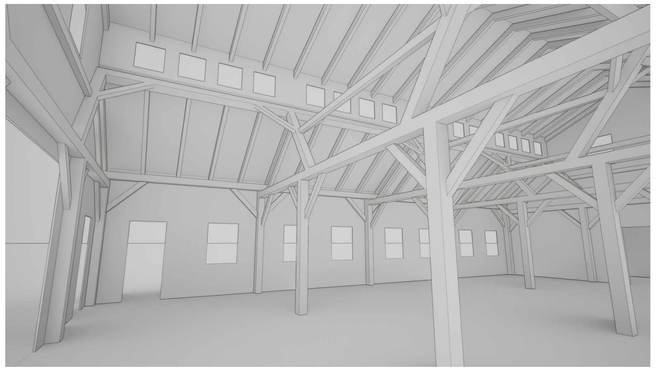

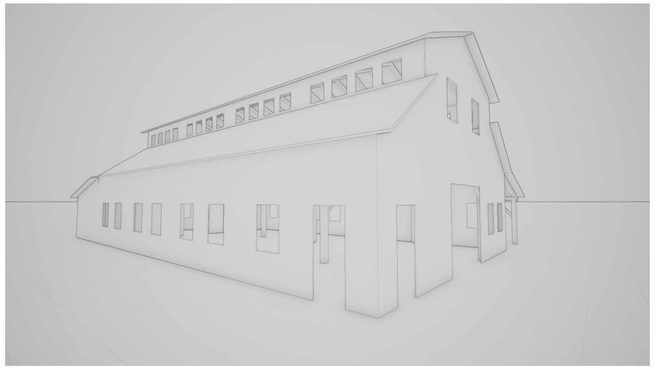

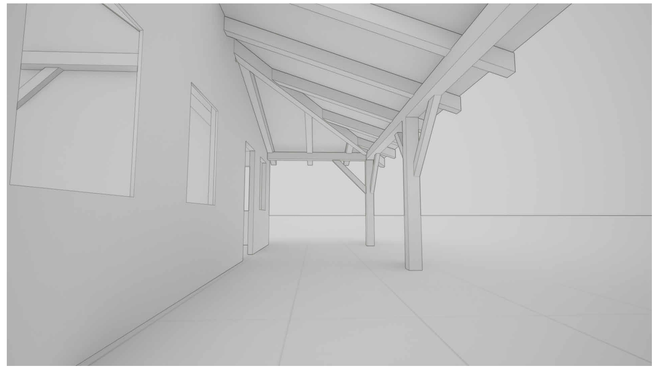

Winter Solstice Noon
at 40.951164, -90.373306

Summer Solstice Noon at
40.951164, -90.373306

FIRMITAS
149 NORTH BROAD ST, STE 1A
GALESBURG, IL 61401
309-315-4747
team@firmitastimber.com

Project Name:
Knox College Pavilion 02

Project Address:
422 S. Academy St.
Galesburg Il, 61401

Sheet List

Number	Name
TF001	Cover
TF101	Plan
TF201	Elevation
TF202	Elevation

Project number	25.0002
Date	7/1/25
Drawn by	MJY

TF001

Scale

7/8/2025 4:19:49 PM

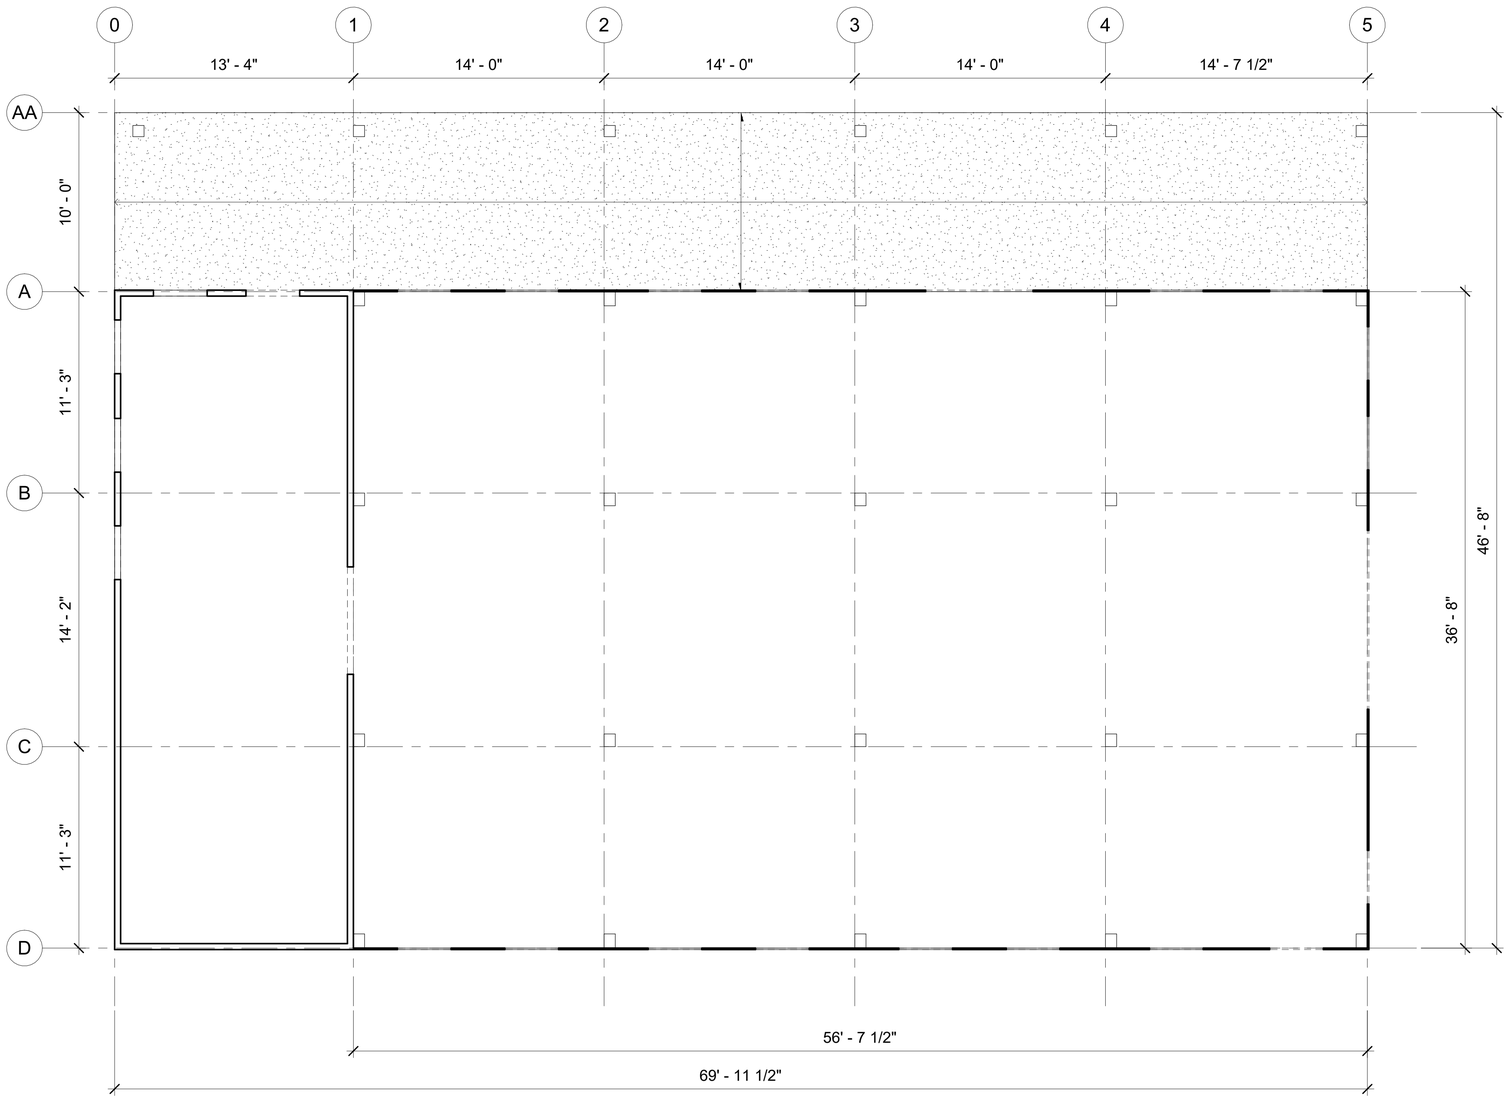

1 Post Plan
1/4" = 1'-0"

FIRMITAS
149 NORTH BROAD ST, STE 1A
GALESBURG, IL 61401
309-315-4747
team@firmitastimber.com

Project Name:
Knox College Pavilion 02

Project Address:
422 S. Academy St.
Galesburg Il, 61401

Project number	25.0002
Date	7/1/25
Drawn by	MJY

TF101

Scale	1/4" = 1'-0"

7/8/2025 4:19:49 PM

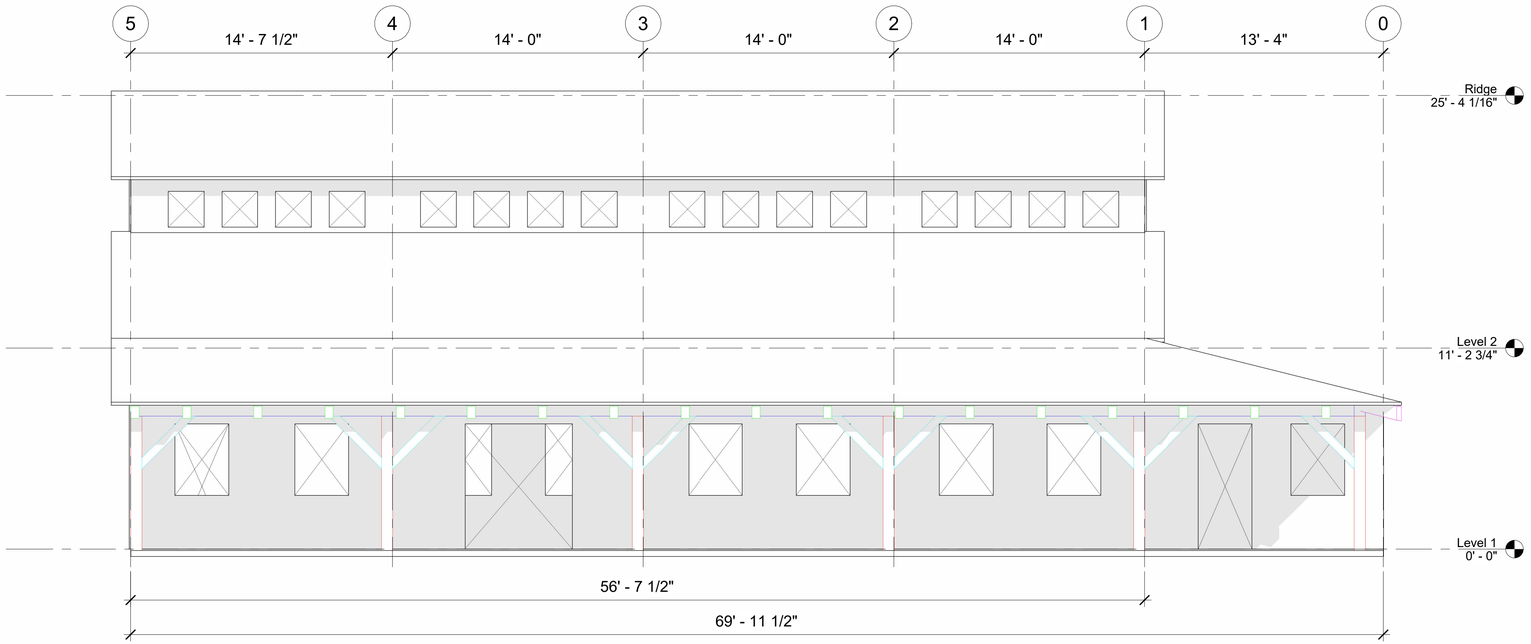

1 North
1/4" = 1'-0"

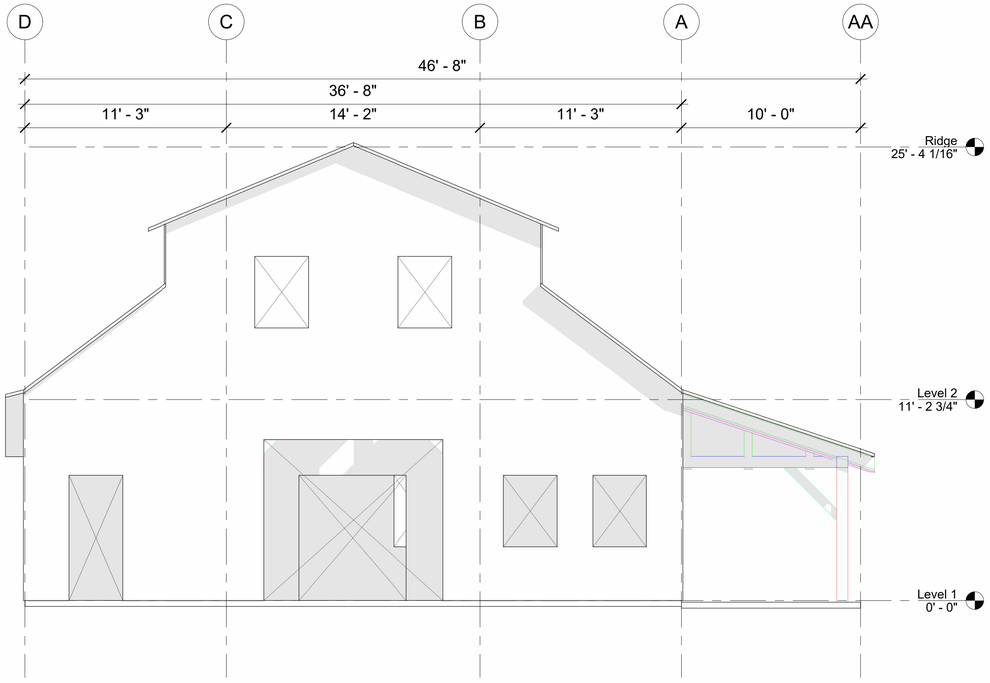

2 East
1/4" = 1'-0"

FIRMITAS
149 NORTH BROAD ST, STE 1A
GALESBURG, IL 61401
309-315-4747
team@firmitastimber.com

Project Name:
Knox College Pavilion 02

Project Address:
422 S. Academy St.
Galesburg Il, 61401

Project number	25.0002
Date	7/1/25
Drawn by	MJY

TF201

Scale	1/4" = 1'-0"

7/8/2025 4:19:53 PM

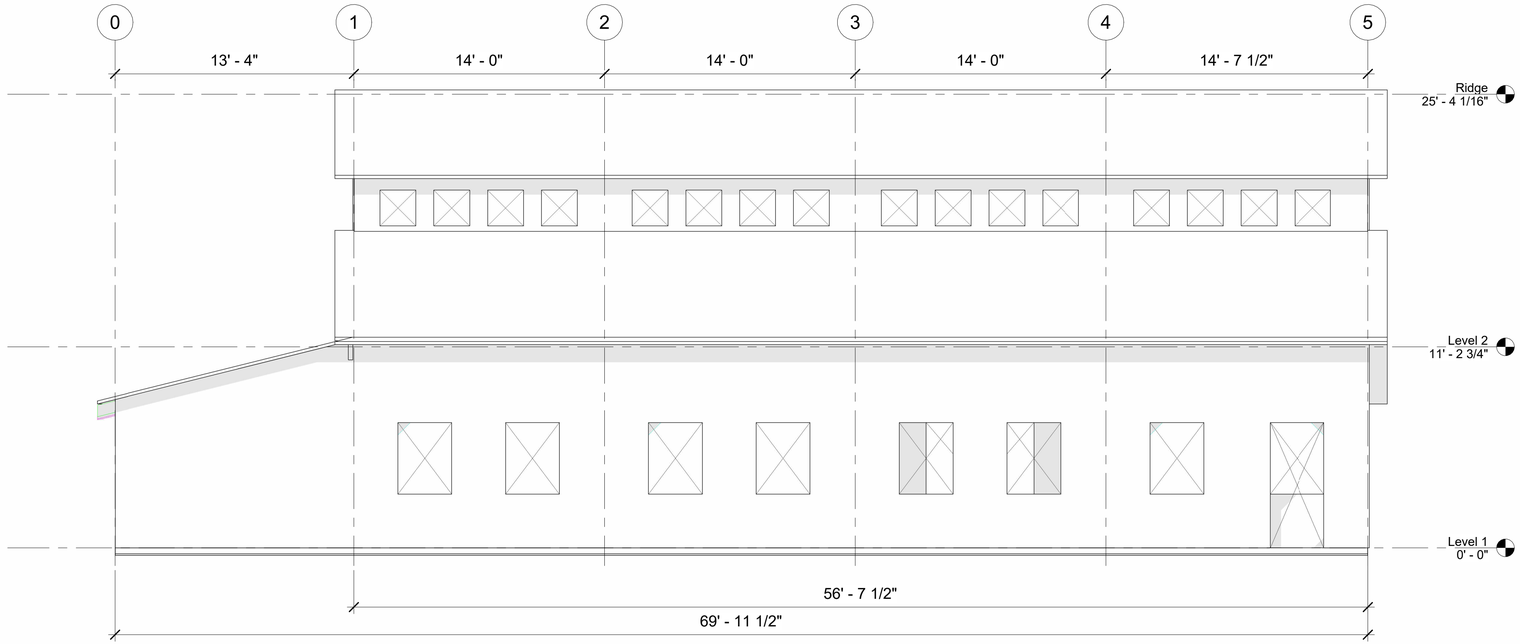

1 South
1/4" = 1'-0"

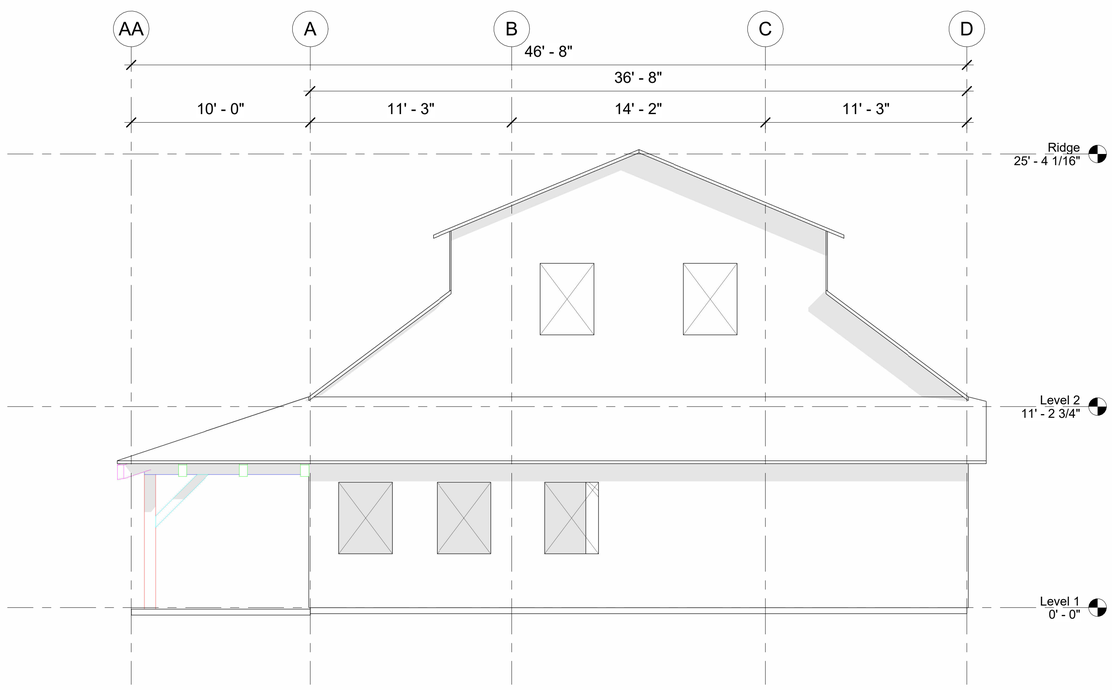

2 West
1/4" = 1'-0"

FIRMITAS
149 NORTH BROAD ST, STE 1A
GALESBURG, IL 61401
309-315-4747
team@firmitastimber.com

Project Name:
Knox College Pavilion 02

Project Address:
422 S. Academy St.
Galesburg Il, 61401

Project number	25.0002
Date	7/1/25
Drawn by	MJY

TF202

Scale	1/4" = 1'-0"

7/8/2025 4:19:57 PM